
BLUEPRINT3D / ARCHITECTURAL TEST SERIES

5 MARLA / COMPACT FAMILY HOUSE

Two bedrooms - separate drawing room - U stair

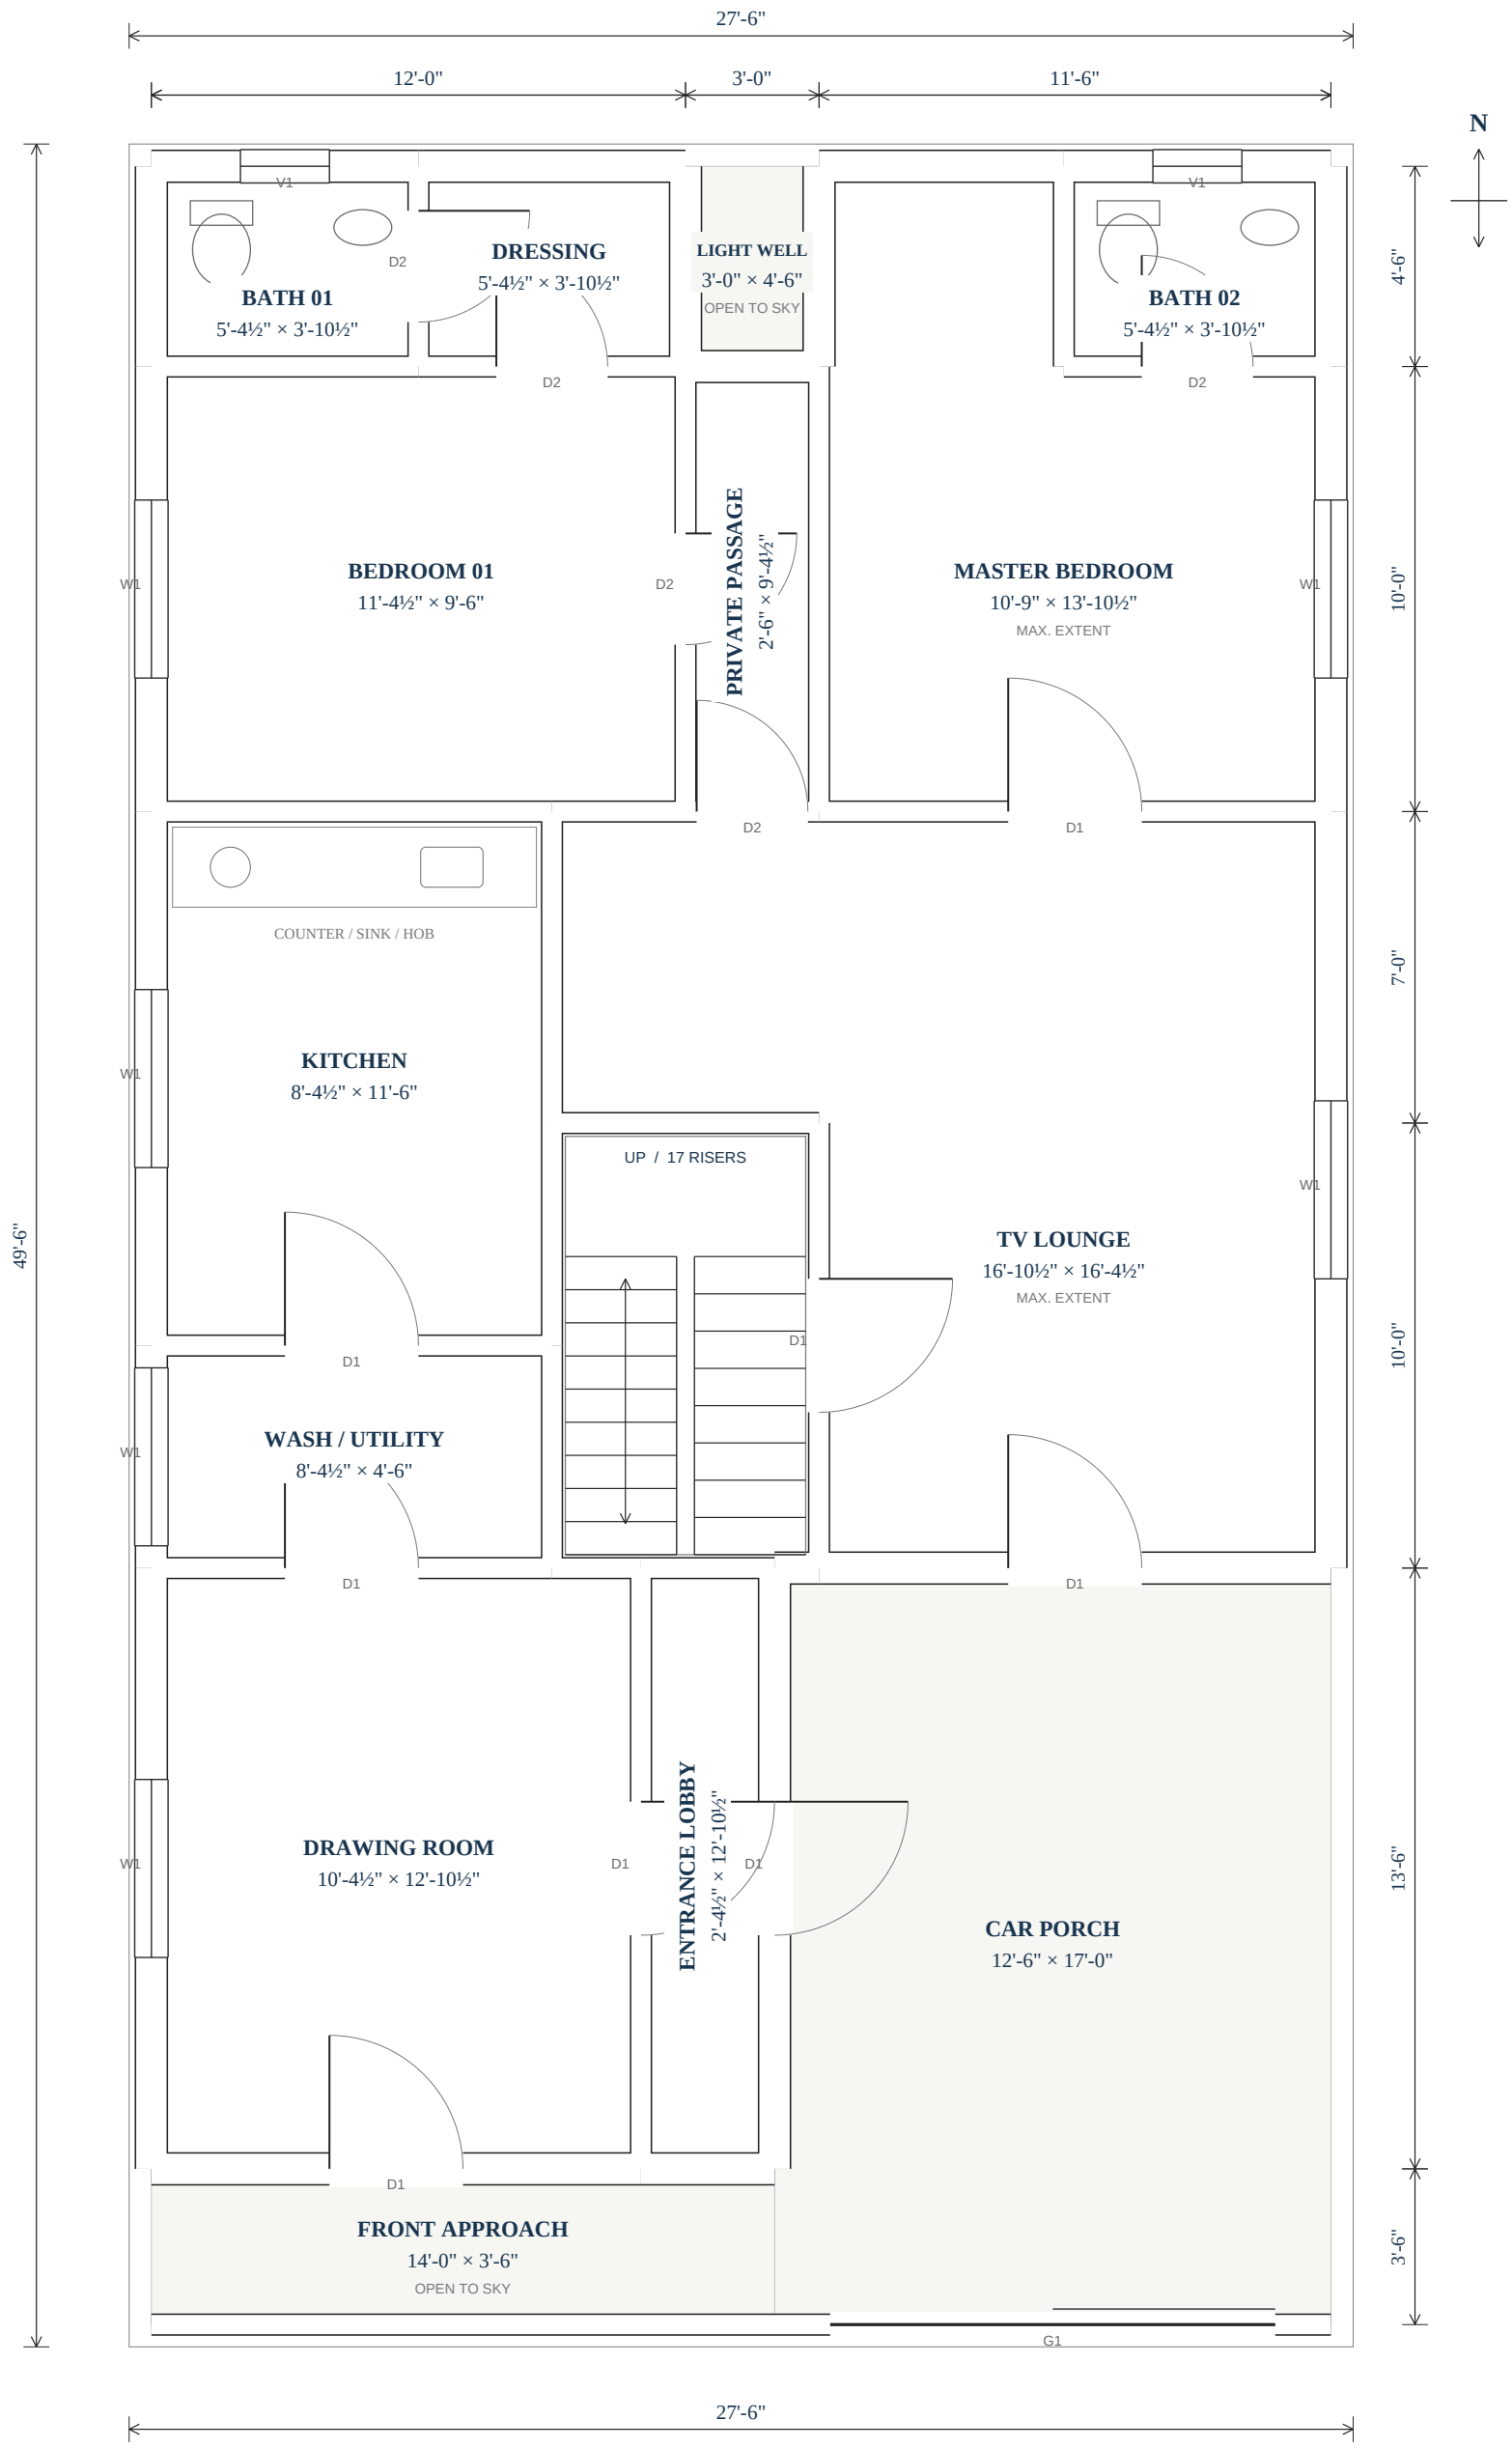

ROAD / STREET FRONT

ARCHITECTURAL RECOGNITION TEST SET

Doors, windows, fixtures, stairs, service spaces and dimension chains are deliberately included.

Concept layouts for app testing. Dimensions and symbols share the supplied editable JSON geometry.

GROUND FLOOR

DIMENSIONED PLAN

DRAWING GF-01

REV A | 15 OCT 2026

PLOT SCHEDULE

27'-6" x 49'-6"

1,361.25 sq ft

5.00 MARLA

2 BEDROOMS

15 NAMED SPACES

SCALE 1:50 ON A3

GENERAL NOTES

All dimensions in feet/inches.

Room labels: clear floor extents.

MAX: irregular room envelope.

Outer chains: wall centre lines.

External walls: 9 inches.

Internal partitions: 6 inches.

Wall height: 9 feet 6 inches.

D1: 3 feet x 7 feet.

D2: 2 feet 6 inches x 7 feet.

W1: 4 feet x 4 feet.

W1 sill: 3 feet above floor.

V1: 2 feet x 2 feet 6 inches.

V1 sill: 4 feet 6 inches.

G1: sliding front gate.

Stair: 17 risers to upper level.

Upper-floor plan not included.

OPENING SCHEDULE

D1	QUANTITY 8
D2	QUANTITY 5
G1	QUANTITY 1
V1	QUANTITY 2
W1	QUANTITY 6

ROOM INDEX

01	BATH 01
02	DRESSING
03	BEDROOM 01
04	LIGHT WELL
05	PRIVATE PASSAGE
06	BATH 02
07	MASTER BEDROOM
08	KITCHEN
09	WASH / UTILITY
10	STAIR HALL
11	TV LOUNGE
12	DRAWING ROOM
13	ENTRANCE LOBBY
14	CAR PORCH
15	FRONT APPROACH


ORIGINAL CONCEPT

APP TEST DRAWING

BLUEPRINT3D / ARCHITECTURAL TEST SERIES

7 MARLA / THREE-BEDROOM HOUSE

Private rear suites - guest bedroom - front drawing room

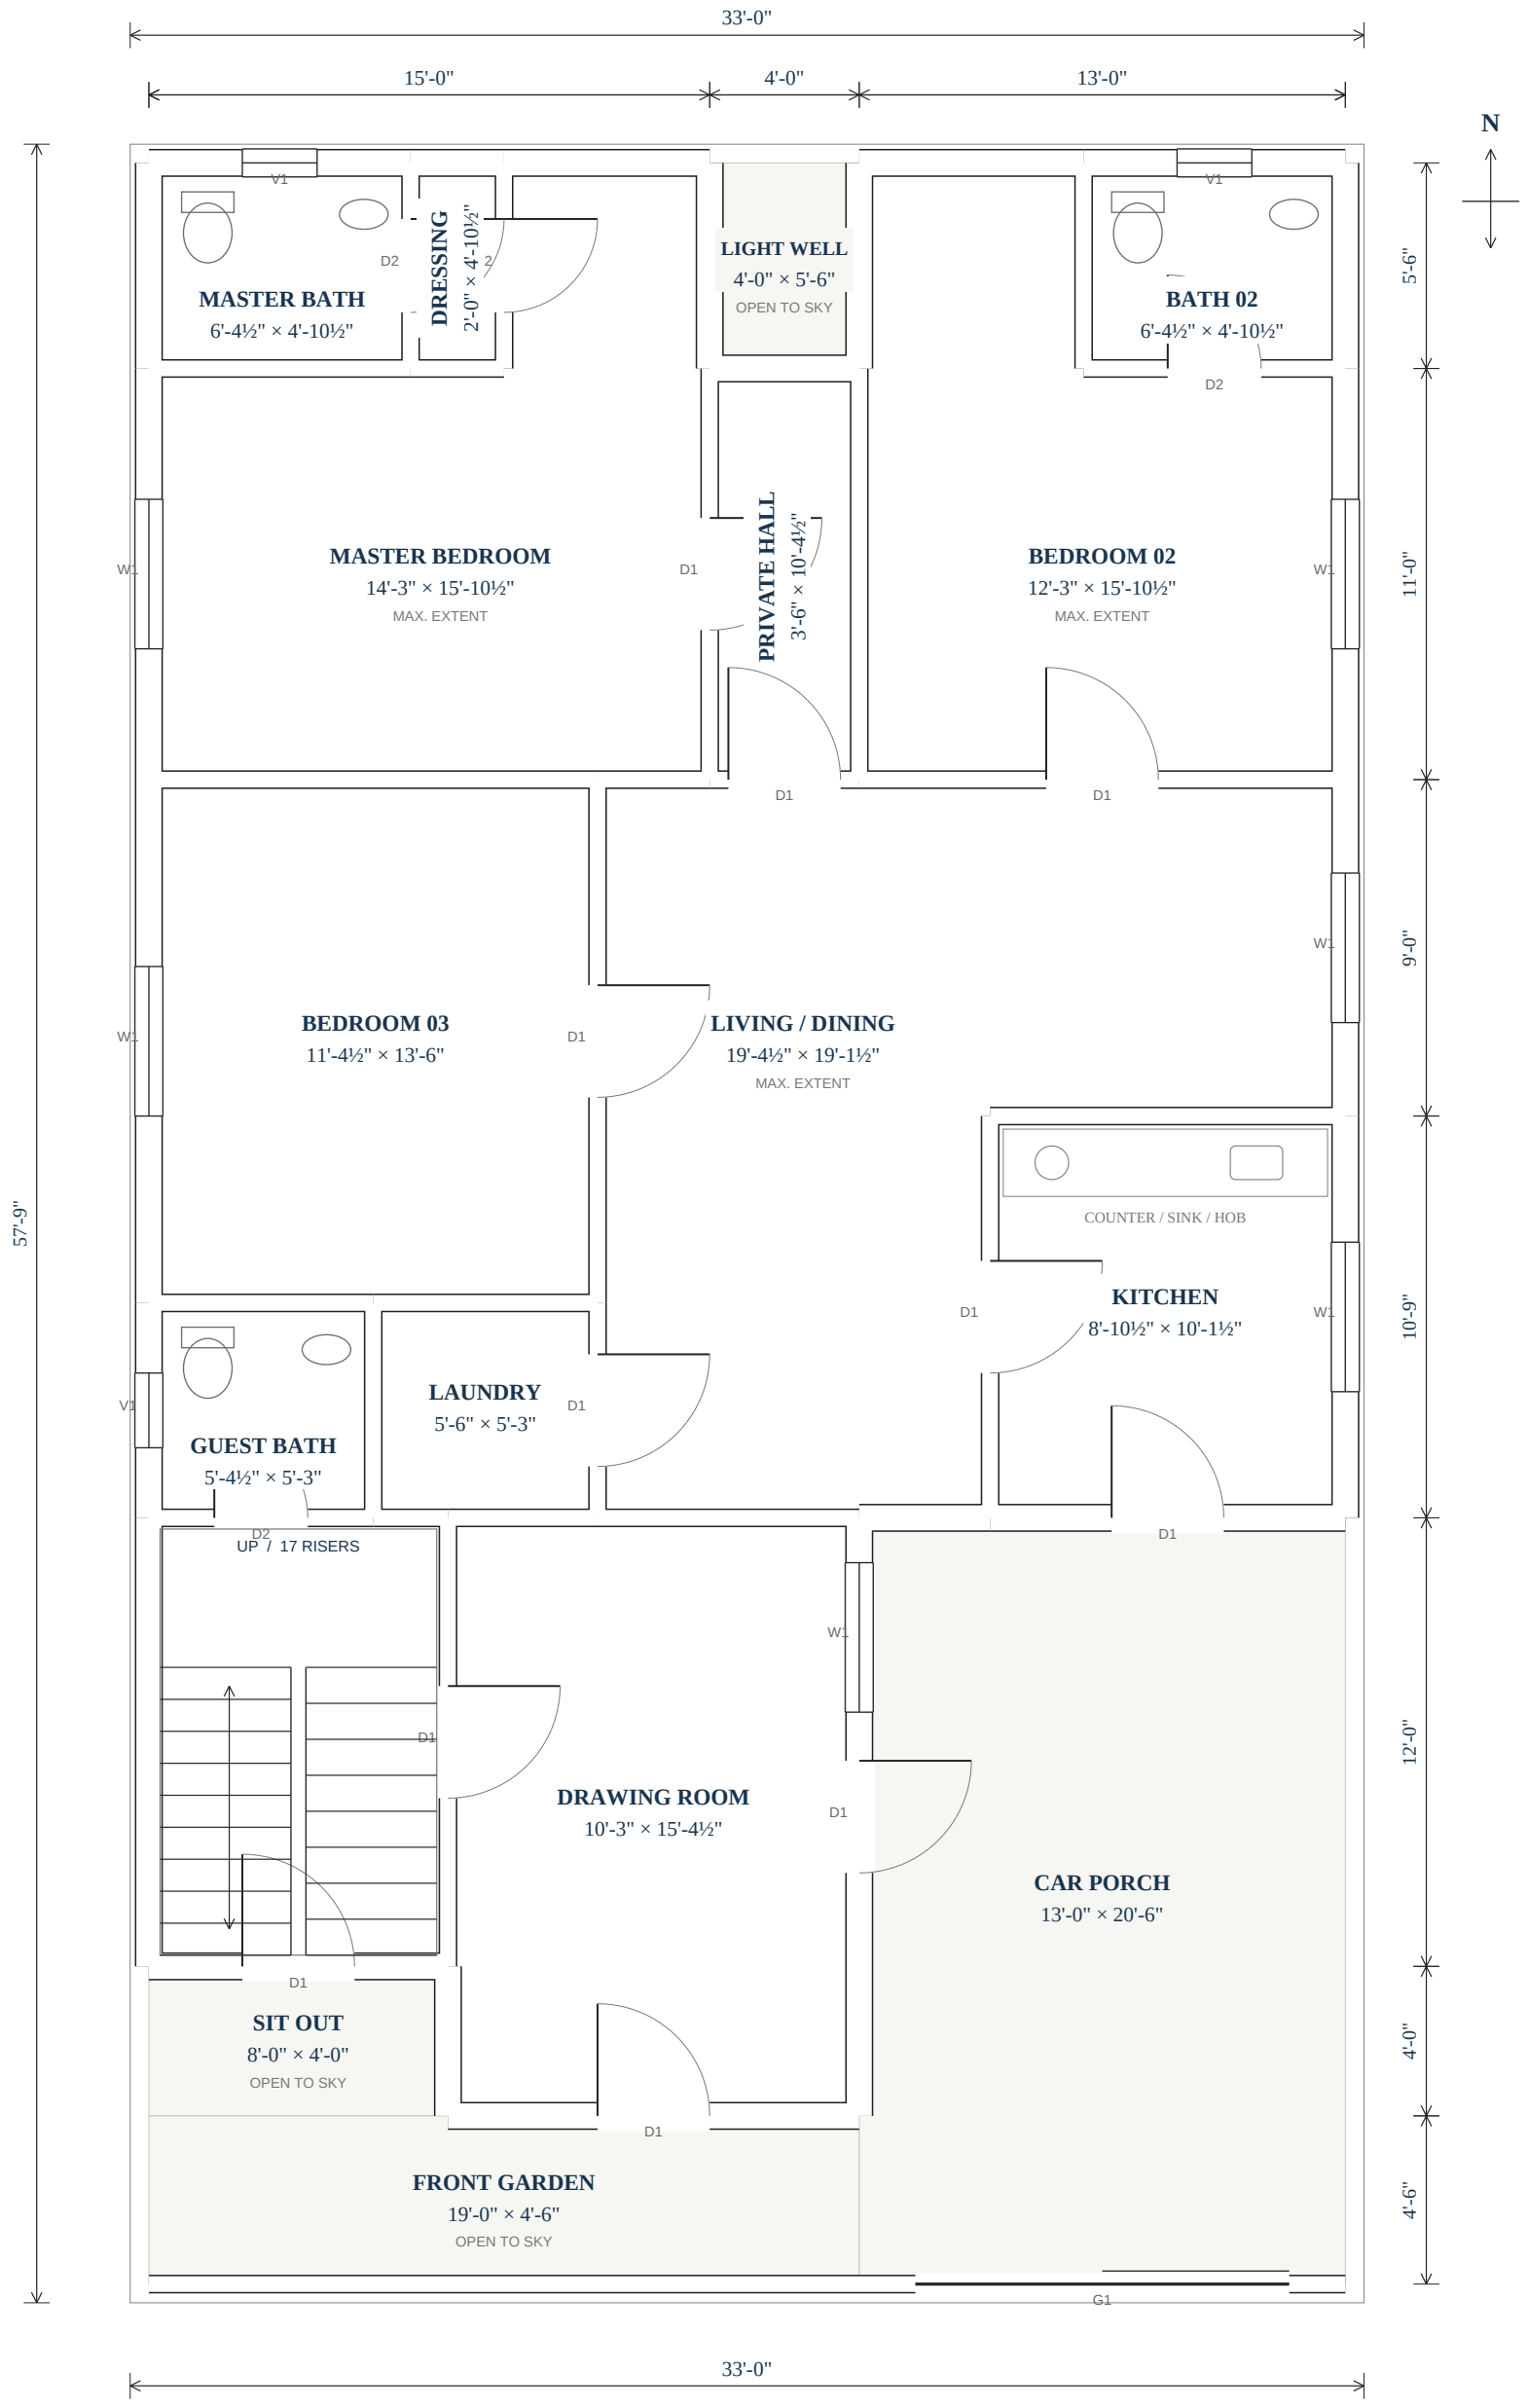

ROAD / STREET FRONT

0.0 2.5 5.0 7.5 10.0 FEET

ARCHITECTURAL RECOGNITION TEST SET

Doors, windows, fixtures, stairs, service spaces and dimension chains are deliberately included.

Concept layouts for app testing. Dimensions and symbols share the supplied editable JSON geometry.

GROUND FLOOR

DIMENSIONED PLAN

DRAWING GF-02

REV A | 15 OCT 2026

PLOT SCHEDULE

33'-0" x 57'-9"

1,905.75 sq ft

7.00 MARLA

3 BEDROOMS

17 NAMED SPACES

SCALE 1:60 ON A3

GENERAL NOTES

All dimensions in feet/inches.

Room labels: clear floor extents.

MAX: irregular room envelope.

Outer chains: wall centre lines.

External walls: 9 inches.

Internal partitions: 6 inches.

Wall height: 9 feet 6 inches.

D1: 3 feet x 7 feet.

D2: 2 feet 6 inches x 7 feet.

W1: 4 feet x 4 feet.

W1 sill: 3 feet above floor.

V1: 2 feet x 2 feet 6 inches.

V1 sill: 4 feet 6 inches.

G1: sliding front gate.

Stair: 17 risers to upper level.

Upper-floor plan not included.

OPENING SCHEDULE

D1	QUANTITY 11
D2	QUANTITY 4
G1	QUANTITY 1
V1	QUANTITY 3
W1	QUANTITY 6

ROOM INDEX

01	MASTER BATH
02	DRESSING
03	MASTER BEDROOM
04	LIGHT WELL
05	PRIVATE HALL
06	BATH 02
07	BEDROOM 02
08	BEDROOM 03
09	GUEST BATH
10	LAUNDRY
11	LIVING / DINING
12	KITCHEN
13	STAIR HALL
14	DRAWING ROOM
15	SIT OUT
16	FRONT GARDEN
17	CAR PORCH


ORIGINAL CONCEPT

APP TEST DRAWING

BLUEPRINT3D / ARCHITECTURAL TEST SERIES

10 MARLA / COURTYARD HOUSE

Three bedrooms - central courtyard - curved stair lobby

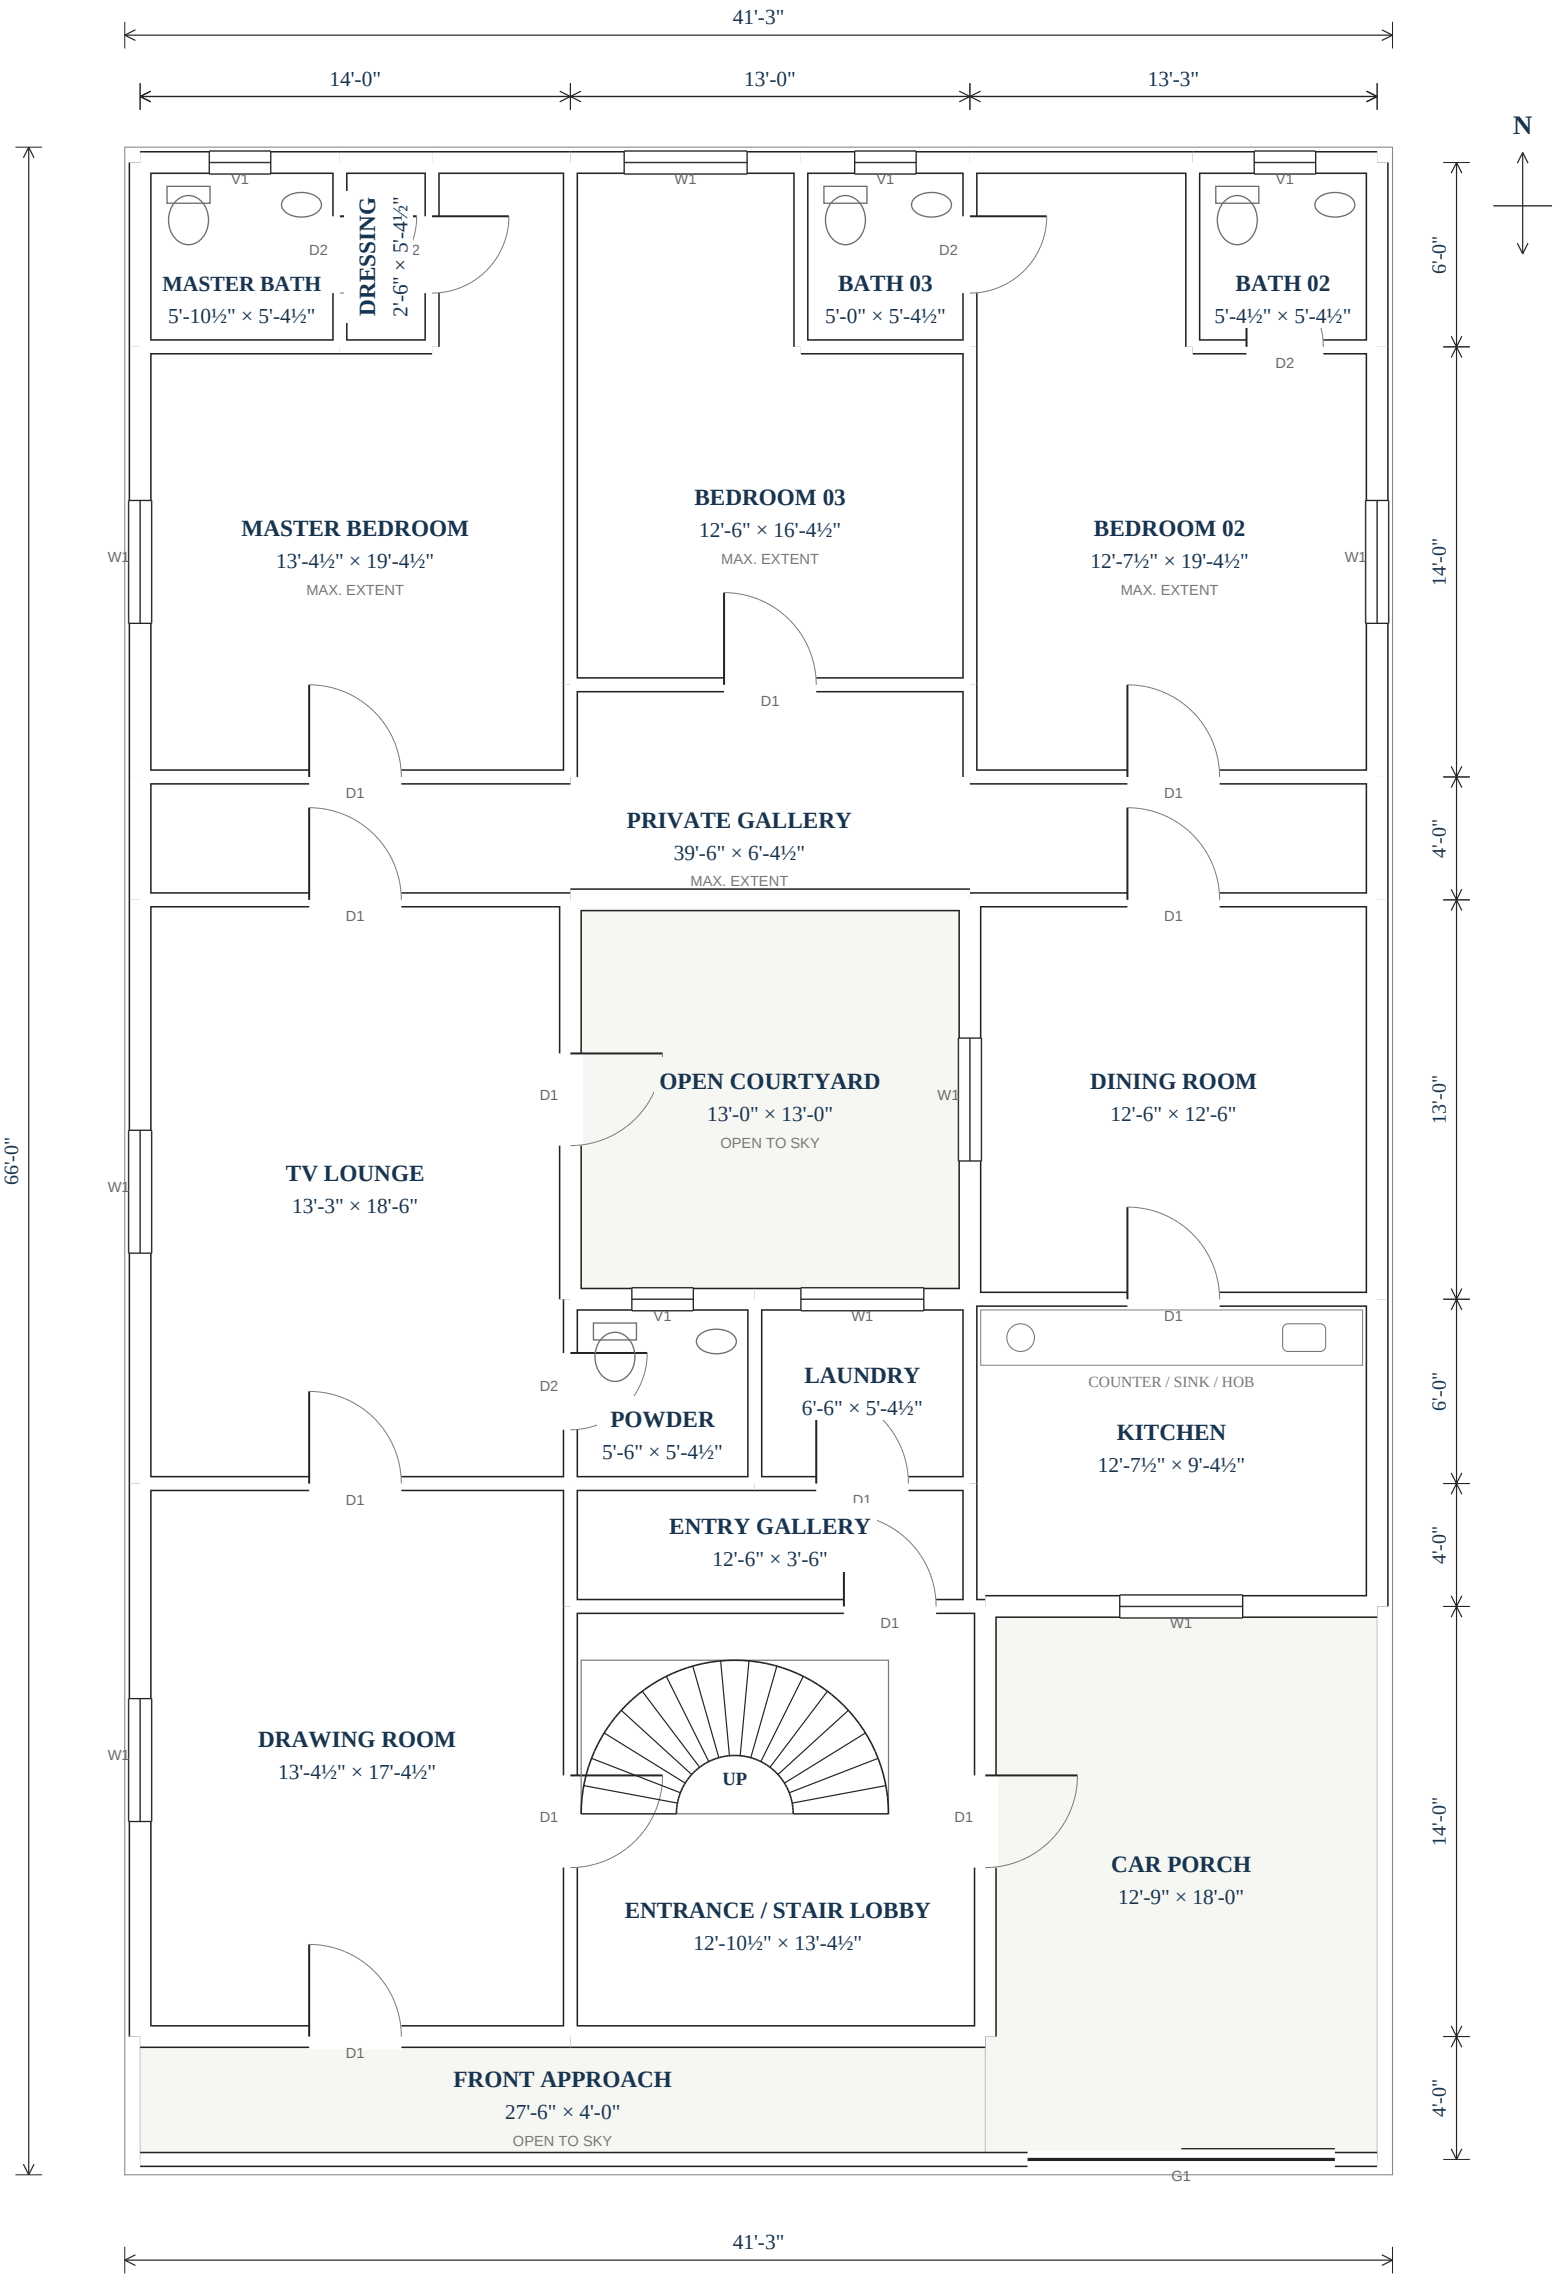

ROAD / STREET FRONT



ARCHITECTURAL RECOGNITION TEST SET

Doors, windows, fixtures, stairs, service spaces and dimension chains are deliberately included.

Concept layouts for app testing. Dimensions and symbols share the supplied editable JSON geometry.

GROUND FLOOR

DIMENSIONED PLAN

DRAWING GF-03

REV A | 15 OCT 2026

PLOT SCHEDULE

41'-3" x 66'-0"

2,722.50 sq ft

10.00 MARLA

3 BEDROOMS

19 NAMED SPACES

SCALE 1:75 ON A3

GENERAL NOTES

All dimensions in feet/inches.

Room labels: clear floor extents.

MAX: irregular room envelope.

Outer chains: wall centre lines.

External walls: 9 inches.

Internal partitions: 6 inches.

Wall height: 9 feet 6 inches.

D1: 3 feet x 7 feet.

D2: 2 feet 6 inches x 7 feet.

W1: 4 feet x 4 feet.

W1 sill: 3 feet above floor.

V1: 2 feet x 2 feet 6 inches.

V1 sill: 4 feet 6 inches.

G1: sliding front gate.

Stair: 17 risers to upper level.

Upper-floor plan not included.

OPENING SCHEDULE

D1	QUANTITY 13
D2	QUANTITY 5
G1	QUANTITY 1
V1	QUANTITY 4
W1	QUANTITY 8

ROOM INDEX

01	MASTER BATH
02	DRESSING
03	MASTER BEDROOM
04	BATH 03
05	BEDROOM 03
06	BATH 02
07	BEDROOM 02
08	PRIVATE GALLERY
09	TV LOUNGE
10	OPEN COURTYARD
11	DINING ROOM
12	KITCHEN
13	POWDER
14	LAUNDRY
15	ENTRY GALLERY
16	DRAWING ROOM
17	ENTRANCE / STAIR LOBBY
18	CAR PORCH
19	FRONT APPROACH


ORIGINAL CONCEPT

APP TEST DRAWING

BLUEPRINT3D / ARCHITECTURAL TEST SERIES

20 MARLA / GARDEN RESIDENCE

Four bedrooms - garden court - study - two-car porch

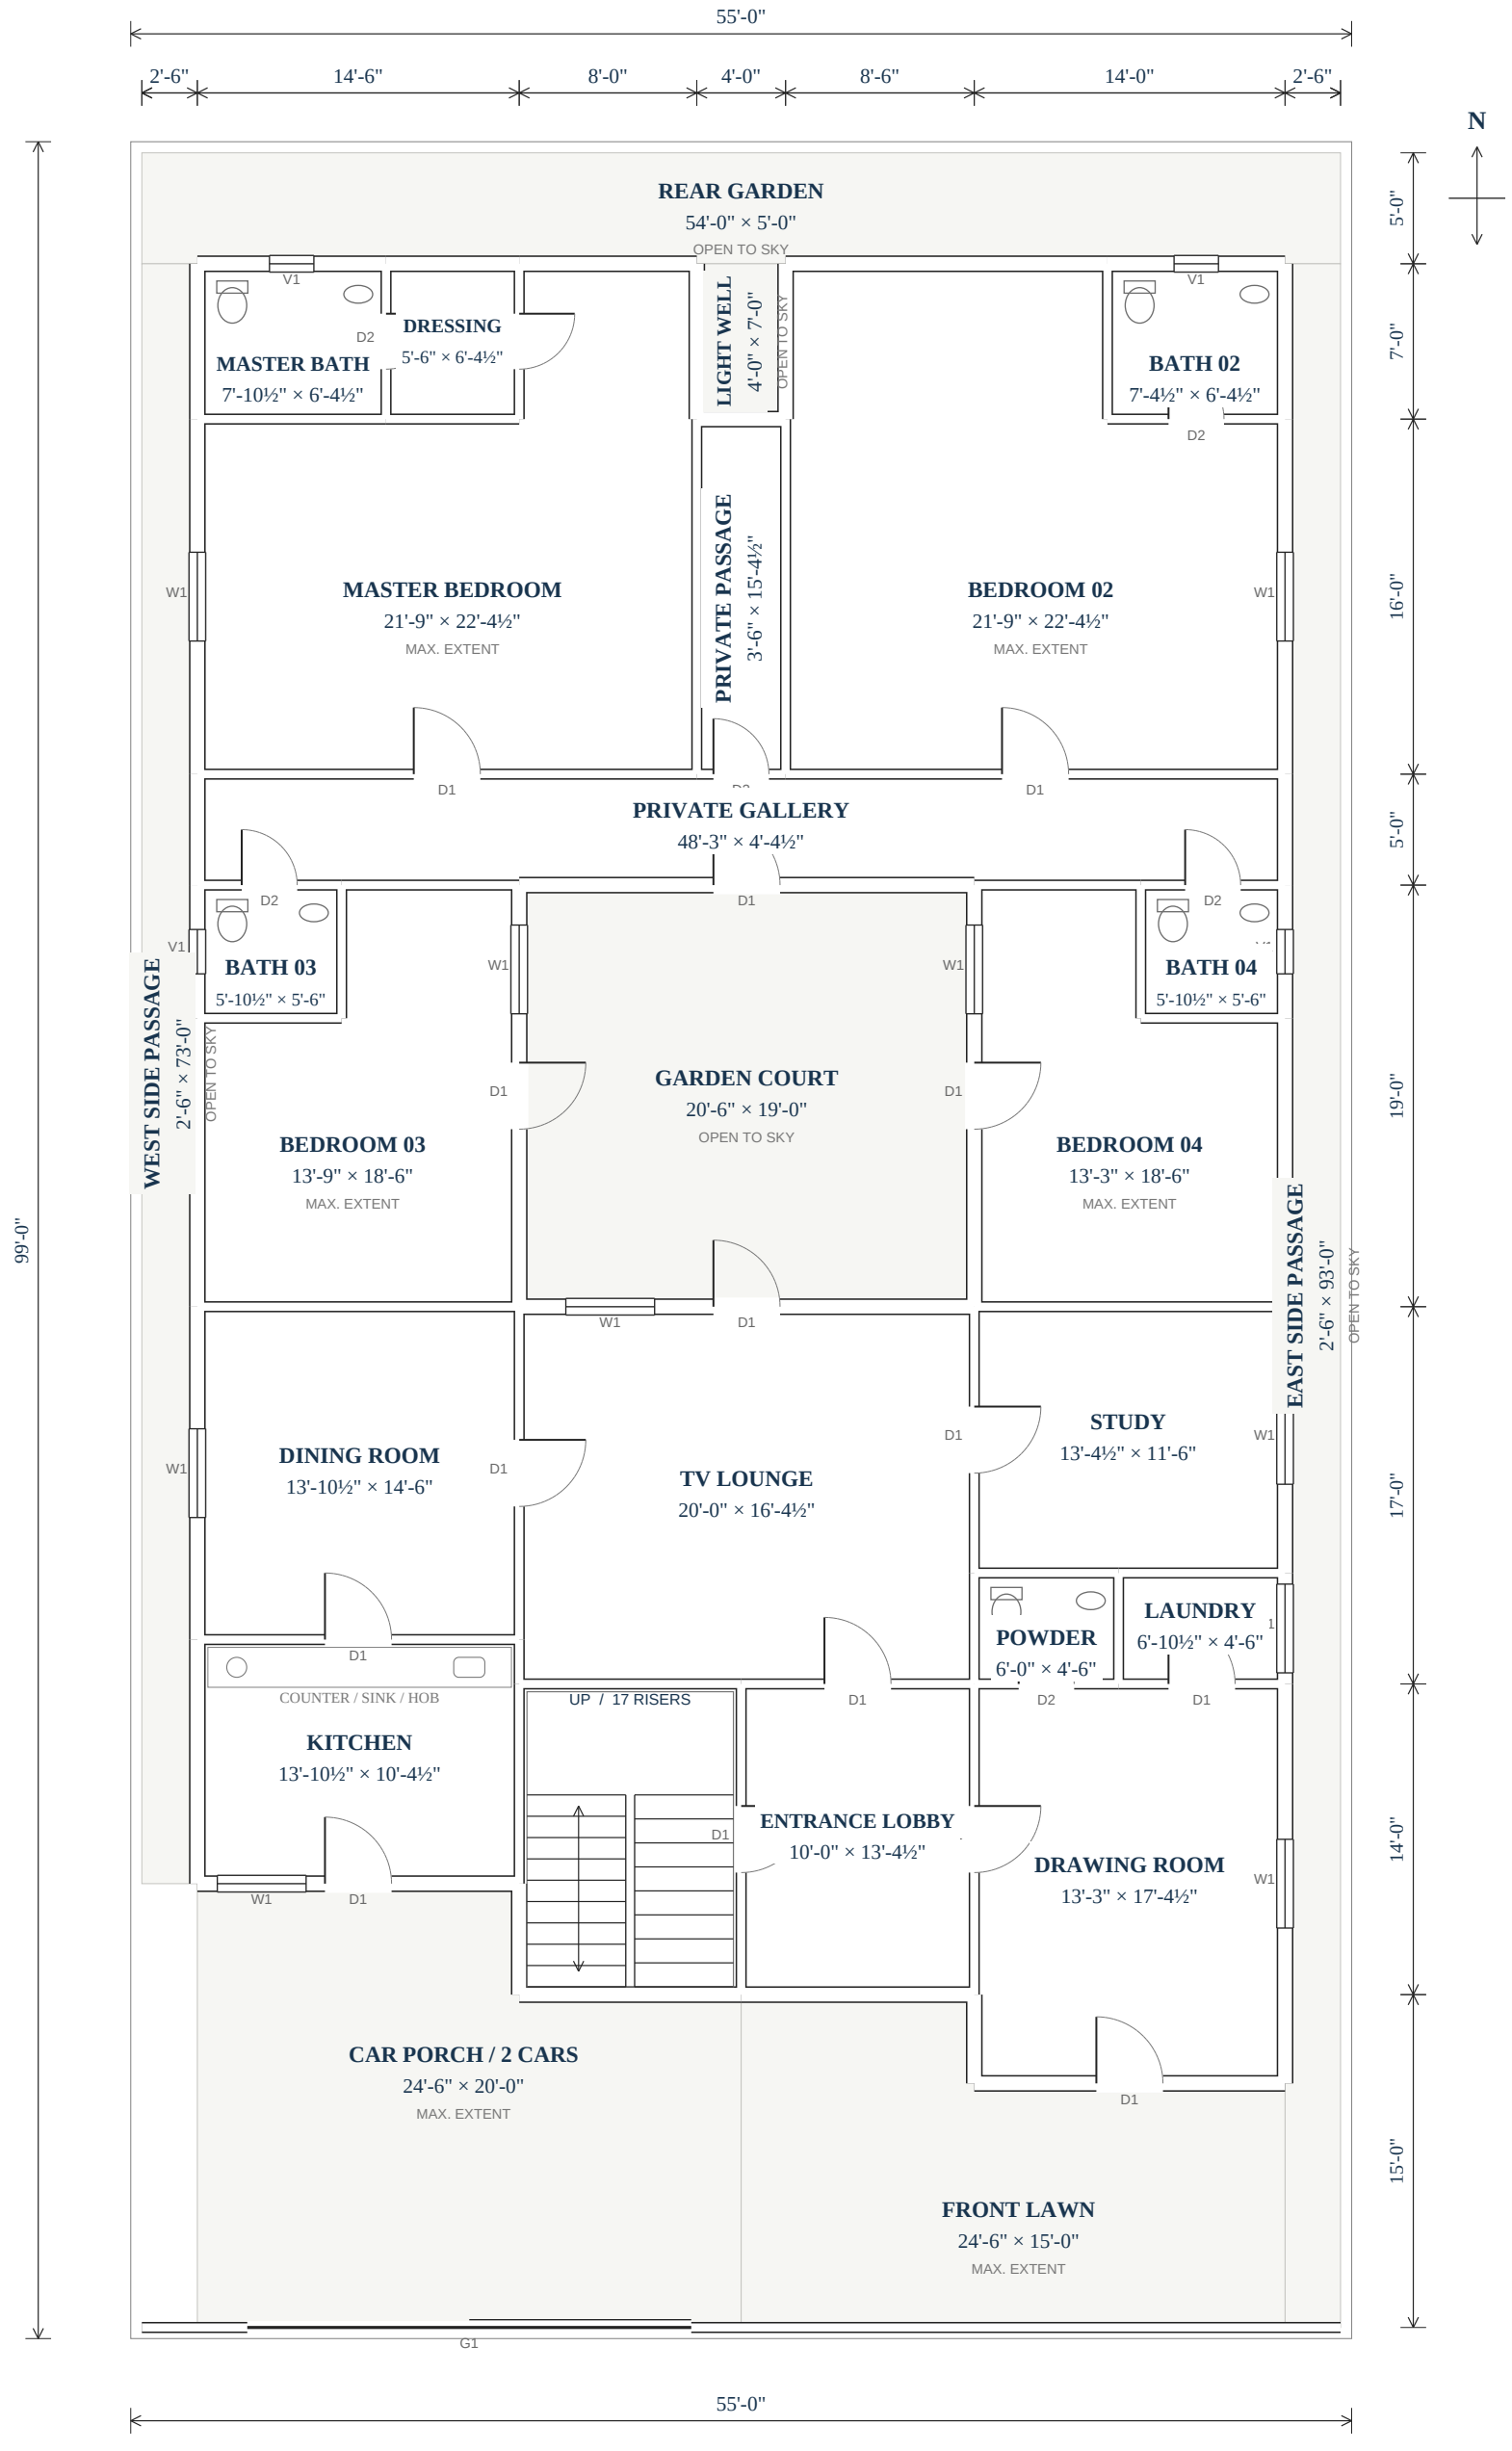

ROAD / STREET FRONT

ARCHITECTURAL RECOGNITION TEST SET

Doors, windows, fixtures, stairs, service spaces and dimension chains are deliberately included.

Concept layouts for app testing. Dimensions and symbols share the supplied editable JSON geometry.

GROUND FLOOR

DIMENSIONED PLAN

DRAWING GF-04

REV A | 15 OCT 2026

PLOT SCHEDULE

55'-0" x 99'-0"

5,445.00 sq ft

20.00 MARLA

4 BEDROOMS

27 NAMED SPACES

SCALE 1:100 ON A3

GENERAL NOTES

All dimensions in feet/inches.

Room labels: clear floor extents.

MAX: irregular room envelope.

Outer chains: wall centre lines.

External walls: 9 inches.

Internal partitions: 6 inches.

Wall height: 9 feet 6 inches.

D1: 3 feet x 7 feet.

D2: 2 feet 6 inches x 7 feet.

W1: 4 feet x 4 feet.

W1 sill: 3 feet above floor.

V1: 2 feet x 2 feet 6 inches.

V1 sill: 4 feet 6 inches.

G1: sliding front gate.

Stair: 17 risers to upper level.

Upper-floor plan not included.

OPENING SCHEDULE

D1	QUANTITY 15
D2	QUANTITY 7
G1	QUANTITY 1
V1	QUANTITY 4
W1	QUANTITY 10

ROOM INDEX

01	REAR GARDEN
02	WEST SIDE PASSAGE
03	EAST SIDE PASSAGE
04	MASTER BATH
05	DRESSING
06	MASTER BEDROOM
07	LIGHT WELL
08	PRIVATE PASSAGE
09	BATH 02
10	BEDROOM 02
11	PRIVATE GALLERY
12	BATH 03
13	BEDROOM 03
14	GARDEN COURT
15	BATH 04
16	BEDROOM 04
17	DINING ROOM
18	KITCHEN
19	TV LOUNGE
20	STUDY
21	POWDER
22	LAUNDRY
23	DRAWING ROOM
24	STAIR HALL
25	ENTRANCE LOBBY
26	CAR PORCH / 2 CARS
27	FRONT LAWN

ORIGINAL CONCEPT

APP TEST DRAWING